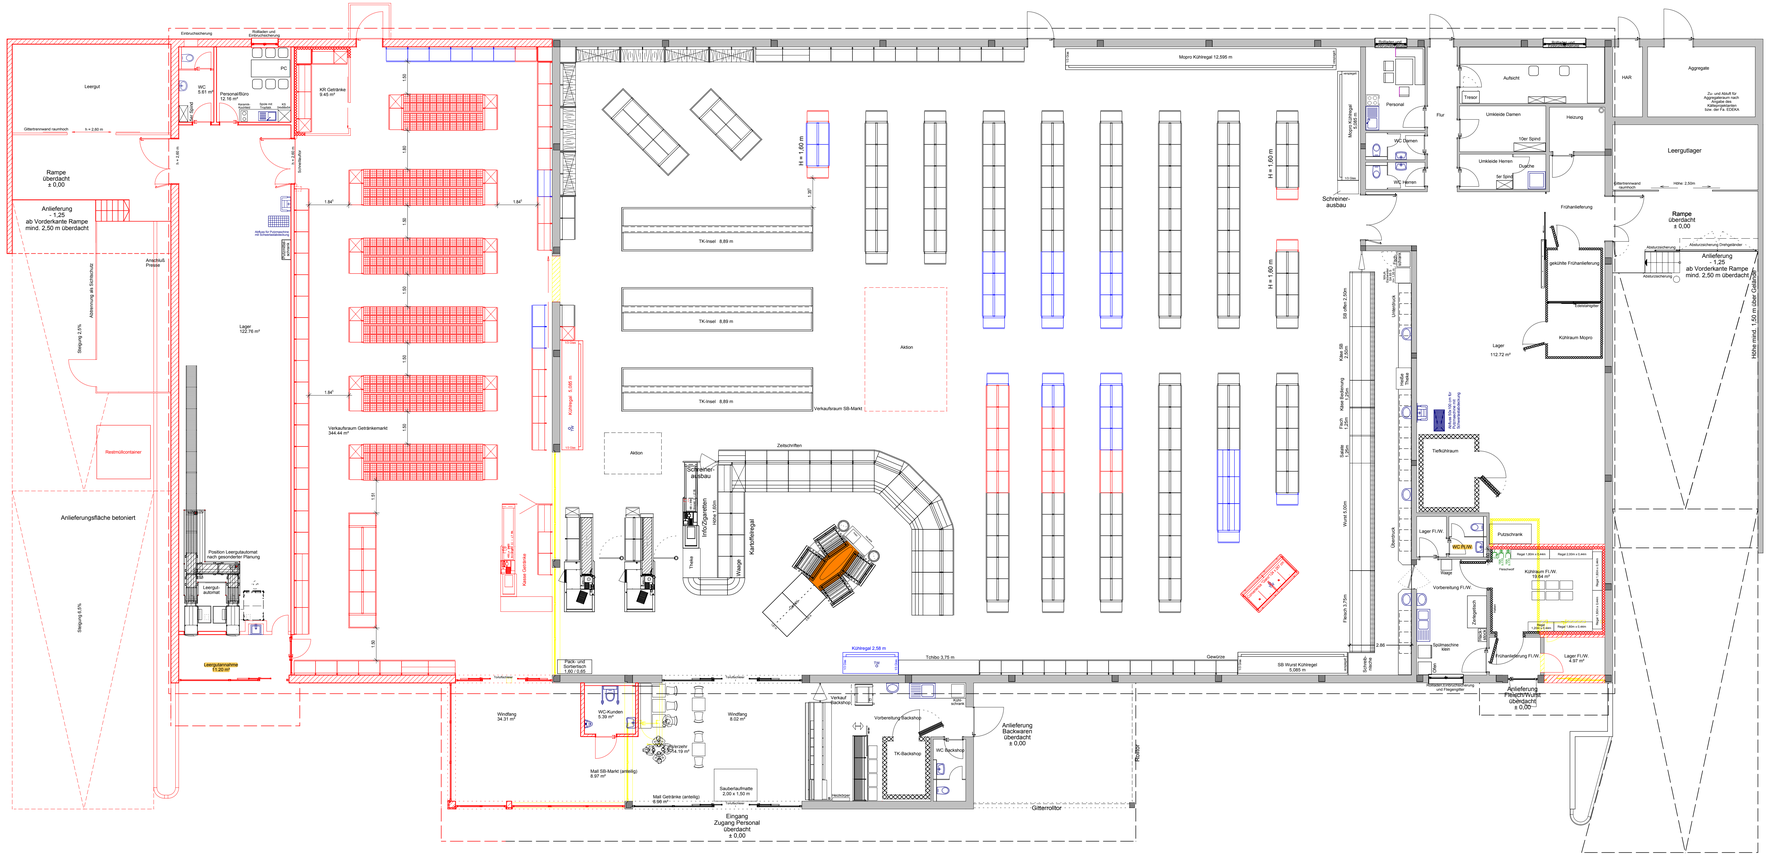

Legende:

- RJ45 Netzwerkdose 1-/2-fach
- für WLAN AccessPoint, DECT Station, ESL (electronic self label) - 1 x Duplexleitung, Deckenbereich
- 1-/2-/3-fach Steckdose 230 V
- CEE Steckdose 230 V
- CEE Steckdose 400 V
- Steckdosen schaltbar
- Bodensteckdose mit Deckel 230 V
- Deckensteckdose 230 V
- Anschluss jeglicher Art 1-, 3-polig
- Herdanschlussdose
- Boden-/ Deckenauslass
- Lautsprecher (mit Regler)
- Schlüsselschalter
- Türkontakt
- Klingeltaster
- Klingel
- Erdungsanschluss
- Elektroverteilung
- Bedientableau
- Drucker/Fax - je 1 x 2-fach RJ45 Netzwerkdose je 1 x 2-fach Steckdose
- Arbeitsplatz - je 2 x 2-fach RJ45 Netzwerkdose je 1 x 2-fach Steckdose je 2 x 3-fach Steckdose
- Strahler Philips CoreLine LED
- Strahler Philips LuxSpace Compact LED
- Einlegeleuchte Philips CoreLine LED
- Deckeneinlegeleuchte Philips CoreView LED
- Langfeldleuchten Philips Maxos LED
- Langfeldleuchte Philips CoreLine LED

- alle Steckdosen im Außen- und Windfangbereich von innen abschaltbar

Sonstiges:

1. Bauliche Anpassungen aufgrund behördlicher Auflagen sind vermieterseits in Abstimmung mit EDEKA zu erbringen.
2. EDEKA behält sich die Möglichkeit der kostenfreien Änderung der Raumaufteilung bis zur Werkplanung vor.
3. Bei der Flächenzusammenstellung sind die Technikräume nicht berücksichtigt.
4. Kühlräume müssen im Rohbeton um die Stärke der Isolierung abgesenkt sein.
5. Zweiflüglige T-30-Türen sind mit Magnetfeststeller und Rauchmelder auszurüsten.
6. Sämtliche Türen sind ohne Bodenanschlag auszuführen.

VORABZUG

C	Hummel	23.02.2017	Getränke, Backwaren, Gondeln, Kühlregal, Tofribo und Convenience geändert bzw. verschoben und neu eingefügt
B	Hummel	01.02.2017	Einrichtung und Wände Kühlraum F/W geändert und Texte ergänzt
A	Hummel	23.01.2017	Grundriss und Einrichtung

Planart
EINRICHTUNGSPLAN

Planbezeichnung
Grundriss Erdgeschoss

Projekt
86925 Fuchstal

Bauort
EDEKA
Bahnhofstraße 26 — Telefon
86925 Fuchstal — Fax

Bauherr
Bahr Immobilien GmbH
Am Waltersbühl 6 — Telefon
88239 Wangen — Fax

Flächenberechnung Bestand n. Aufmaß v. 23.07.2014, Erweterung ohne Putzabzug

Regalierung gesamt	...	lfdm	Verkaufsfläche SB-Markt Bestand	ca.	1193,06 m²
Gondelköpfe	...	lfdm	Nebenräume Bestand	ca.	294,13 m²
Obst und Gemüse	...	lfdm	Technikräume Bestand	ca.	25,98 m²
			Gesamtfläche SB-Markt Bestand	ca.	1513,17 m²
Thekenlänge	...	lfdm			
Kühlregal	...	lfdm	Verkaufsfläche SB-Markt u. Getränkemarkt nach Erweterung	ca.	1597,07 m²
			Nebenräume SB-Markt u. Getränkemarkt nach Erweterung	ca.	436,10 m²
TK-Insel	...	lfdm	Technikräume nach Erweterung	ca.	25,98 m²
			Gesamtfläche SB-Markt u. Getränkemarkt nach Erweterung	ca.	2059,15 m²
Getränke	...	lfdm			

EDEKA Handelsgesellschaft Südbayern mbH
Ingolstädter Straße 120
85080 Gaimersheim

Maßstab 1:100
Datum 23.02.2017
Index C

H/B = 594 / 1189 (0.71m²)

Allplan 2013